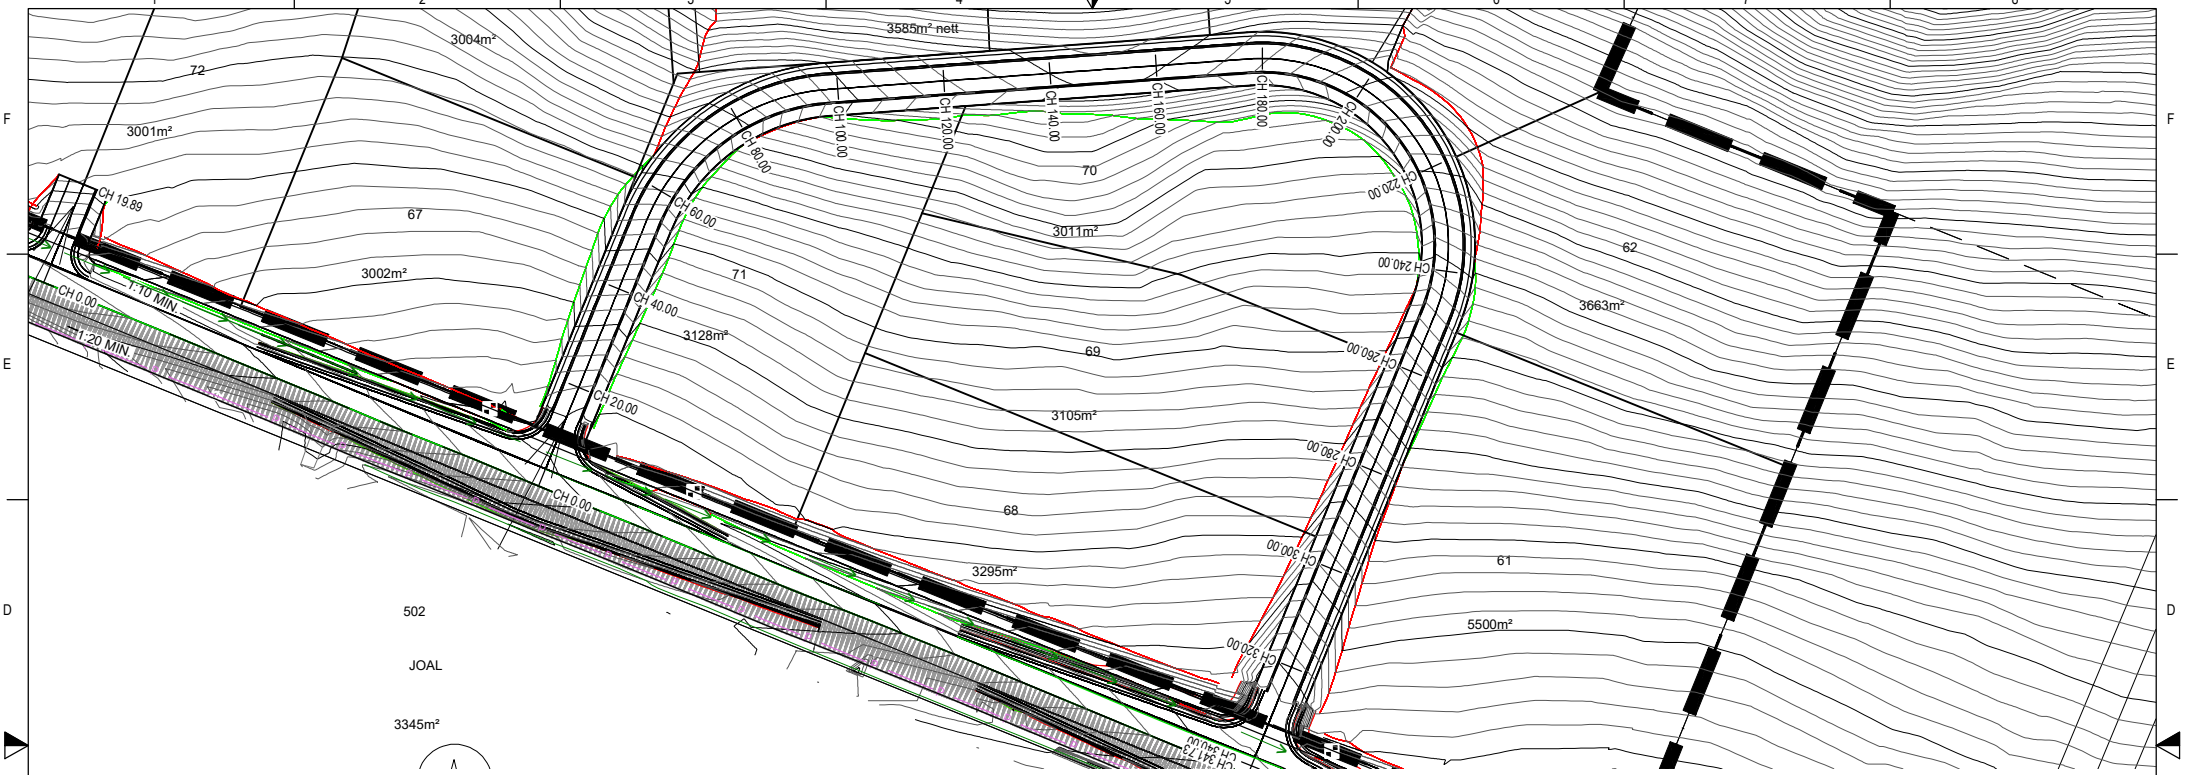

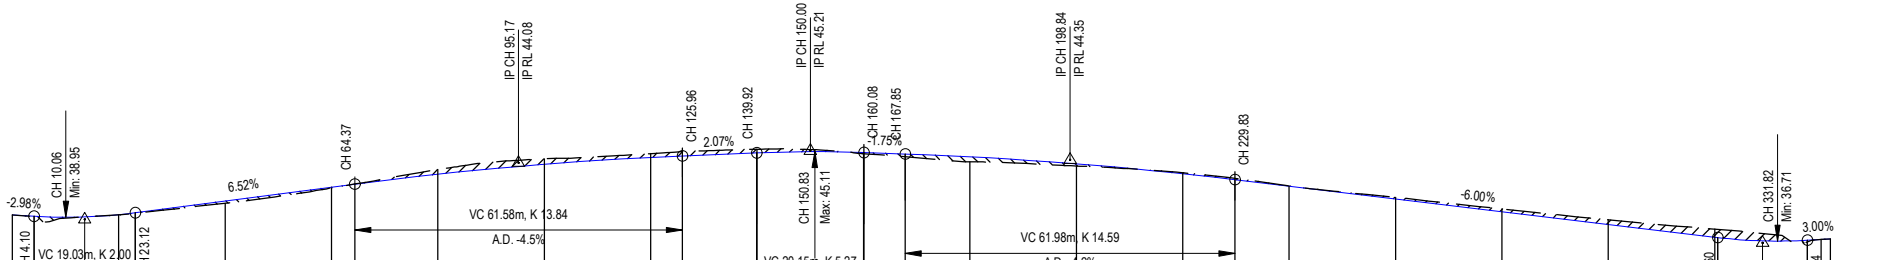

Datum 30.000

DESIGN LEVEL	39.165	39.043		39.200	39.380	40.480	41.784	42.069	42.999	43.933	44.577	44.713	45.002	45.003	45.035	45.034	44.897	44.634	43.980	43.051	42.495	41.885	40.885	39.485	38.285	37.085	37.049		36.796	36.873	36.925
EXISTING LEVEL	39.16	38.902	IP CH 13.31 IP RL 38.76	39.171	39.327	40.271	41.710	42.083	43.436	44.44	44.938	45.134	45.342	45.343	44.918	44.916	44.657	44.169	43.78	43.143	42.611	41.888	40.818	39.744	38.73	37.838	37.815	IP CH 329.02 IP RL 36.54	36.646	36.865	36.925
CUT/FILL (-/+)	0.000	0.141		0.029	0.053	0.209	0.074	-0.015	-0.437	-0.506	-0.361	-0.422	-0.341	-0.340	0.117	0.117	0.240	0.465	0.204	-0.092	-0.116	-0.003	-0.134	-0.259	-0.443	-0.753	-0.766		0.151	0.008	0.000
CHAINAGE	0.000	4.097		20.000	23.122	40.000	60.000	64.375	80.000	100.000	120.000	125.957	139.923	140.000	160.000	160.077	167.853	180.000	200.000	220.000	229.831	240.000	260.000	280.000	300.000	320.000	328.597		337.437	340.000	341.735

FOR ENGINEERING PLAN APPROVAL

Rev	Date	Description	By	Checked
A	19/08/2025	FOR ENGINEERING PLAN APPROVAL	AS	JP

DWG Joal 502
Stage 3
Longitudinal Section

A3 SCALE H1000 V500 — 0 20m 50m

Date 04/04/2025

Drawn AS | Checked JP | Approved JP

File T:\CLIENTS\NEIL CONSTRUCTION LTD\JOBS\18 295 - RANGITANE RIVER PARK STAGE 3\ENGINEERING\DRAWINGS\20\18 295 ST3 - ROAD WORKING.DWG

[redacted]

6 Fairway Drive
Kerikeri, BOI
T: 09 407 8327
F: 09 407 8378
E: info@haighworkman.co.nz

DIMENSIONS MUST NOT BE SCALE MEASURED FROM THESE DRAWINGS. THE CONTRACTOR SHALL CHECK & VERIFY ALL DIMENSIONS INCLUDING, SITE LEVELS, HEIGHTS AND ANGLES ON SITE PRIOR TO COMMENCING ANY WORK. THE COPYRIGHT TO THESE DRAWINGS AND ALL PARTS THERE OF REMAIN THE PROPERTY OF HAIGH WORKMAN LTD. ©2020

Project [redacted]

Client [redacted]

[redacted]

RC no.

Stage

Dwg No. ST3-L06

Sheet No. 14 of 35