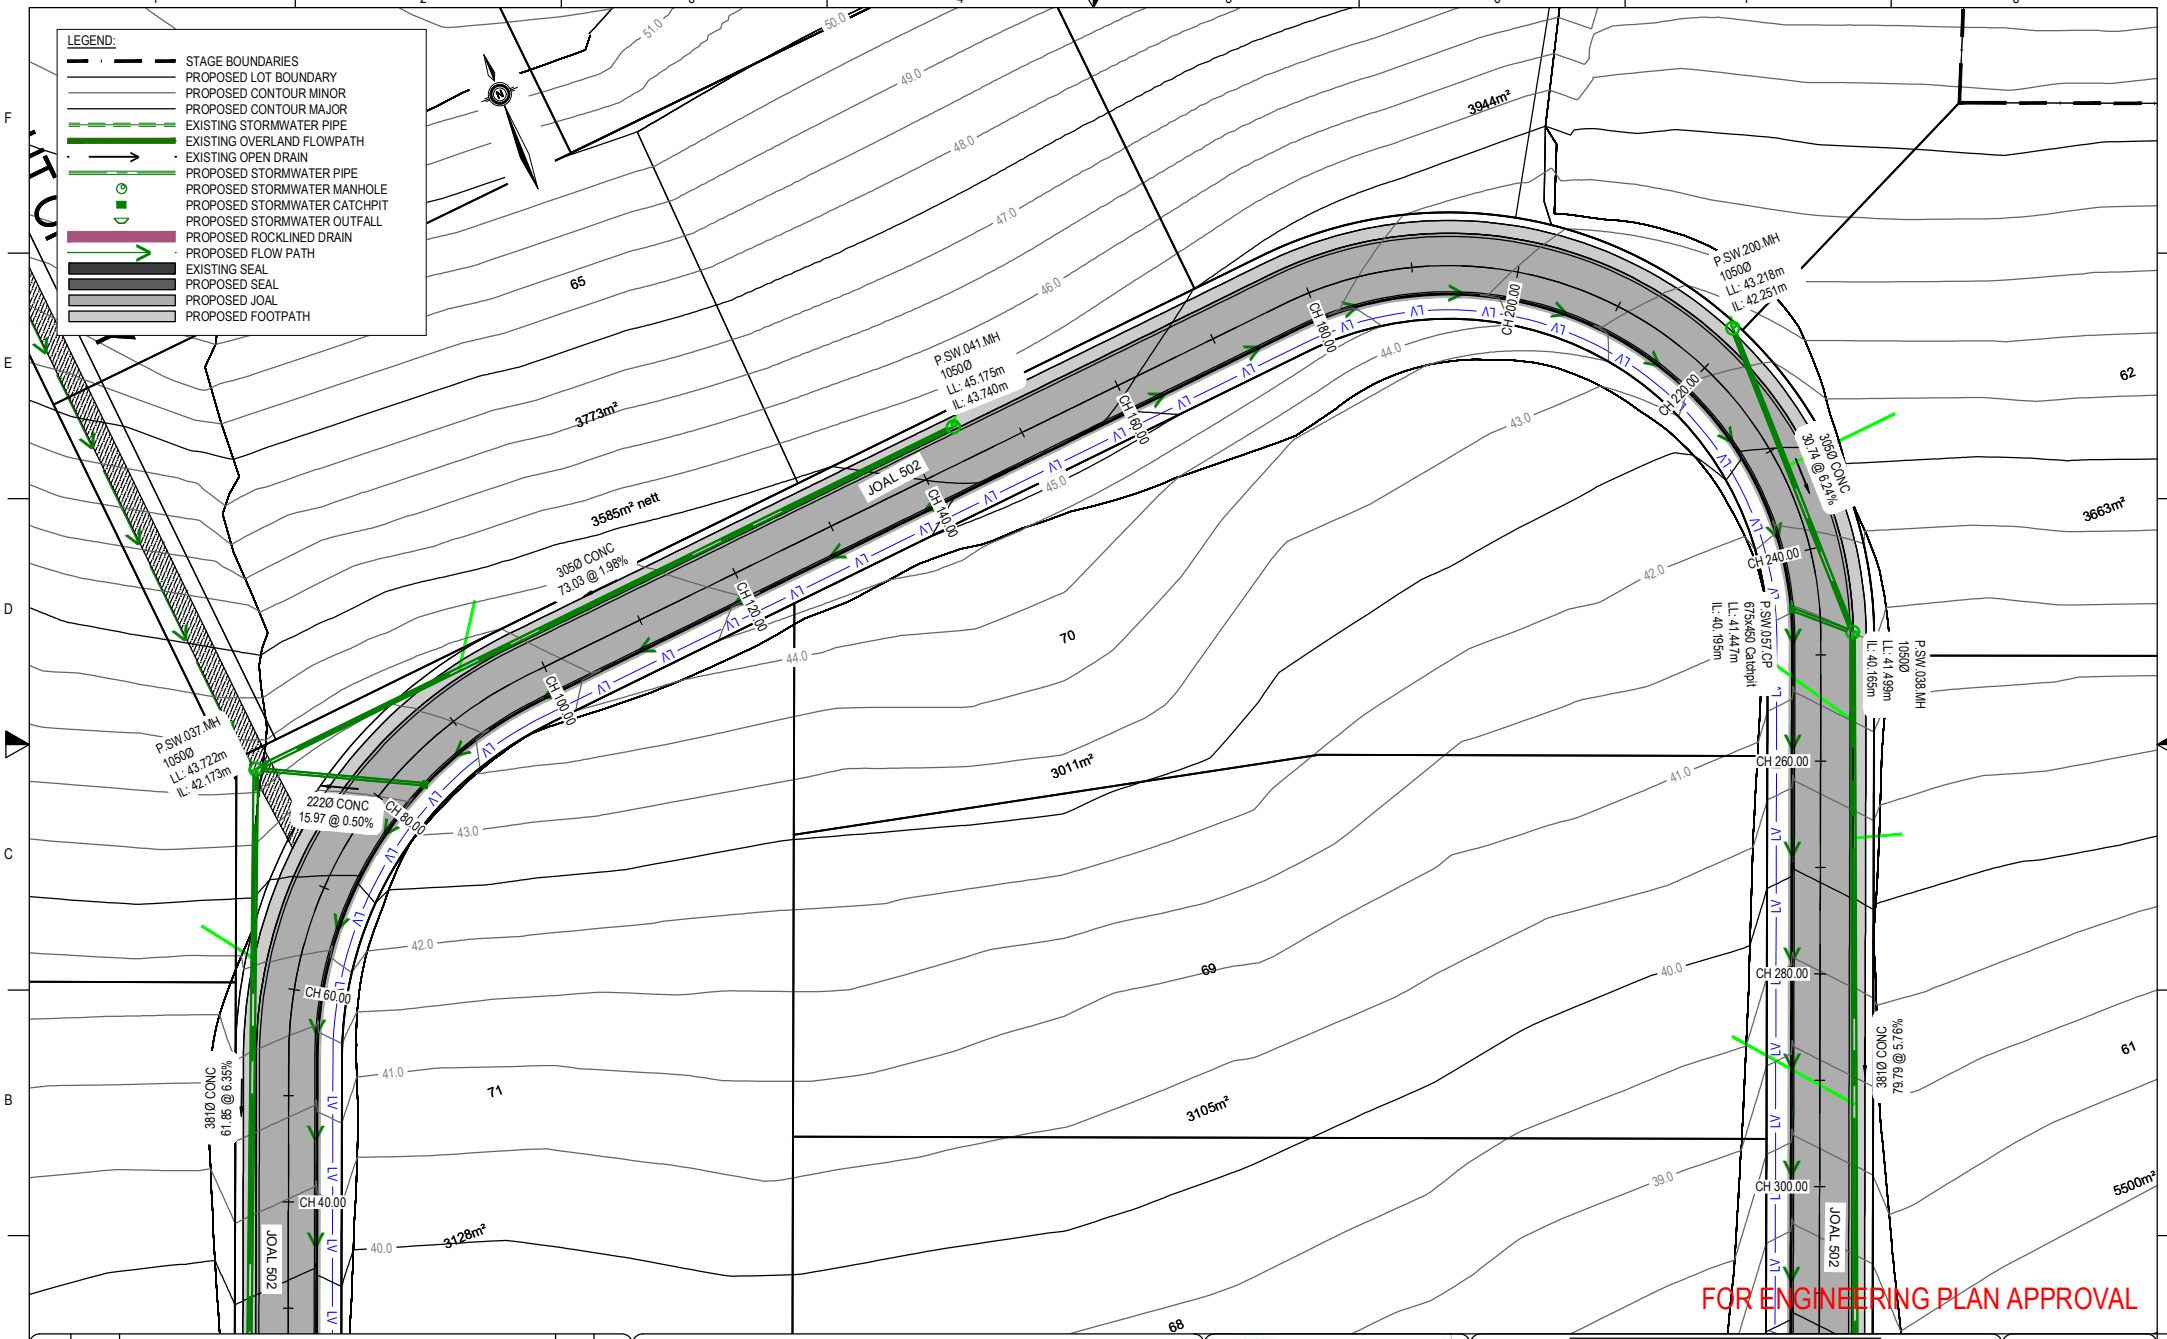

Rev	Date	Description	By	Checked
A	19/08/2025	FOR ENGINEERING PLAN APPROVAL	AS	JP

DWG Joal 502
Stage 3

A3 Scale 1: 500 (0 10 25)

Date 04/04/2025

Drawn AS | Checked JP | Approved JP

File T:\CLIENTS\NEIL CONSTRUCTION LTD\JOBS\18 295 - RANGITANE RIVER PARK STAGE 3\ENGINEERING\DRAWINGS\ENGINEERING PLAN\ST3\STAGE 3\ST3-P07 - GRADING - STAGE_3.DWG

[redacted]

6 Fairway Drive
Kerikeri, BOI

T: 09 407 8327
F: 09 407 8378
E: info@haighworkman.co.nz

DIMENSIONS MUST NOT BE SCALE MEASURED FROM THESE DRAWINGS. THE CONTRACTOR SHALL CHECK & VERIFY ALL DIMENSIONS INCLUDING SITE LEVELS, HEIGHTS AND ANGLES ON SITE PRIOR TO COMMENCING ANY WORK. THE COPYRIGHT TO THESE DRAWINGS AND ALL PARTS THERE OF REMAIN THE PROPERTY OF HAIGH WORKMAN LTD. 62020

Project [redacted]

Client [redacted]

Project No [redacted]

RC no.

Stage

Dwg No. ST3-P07

Sheet No. 8 of 35